
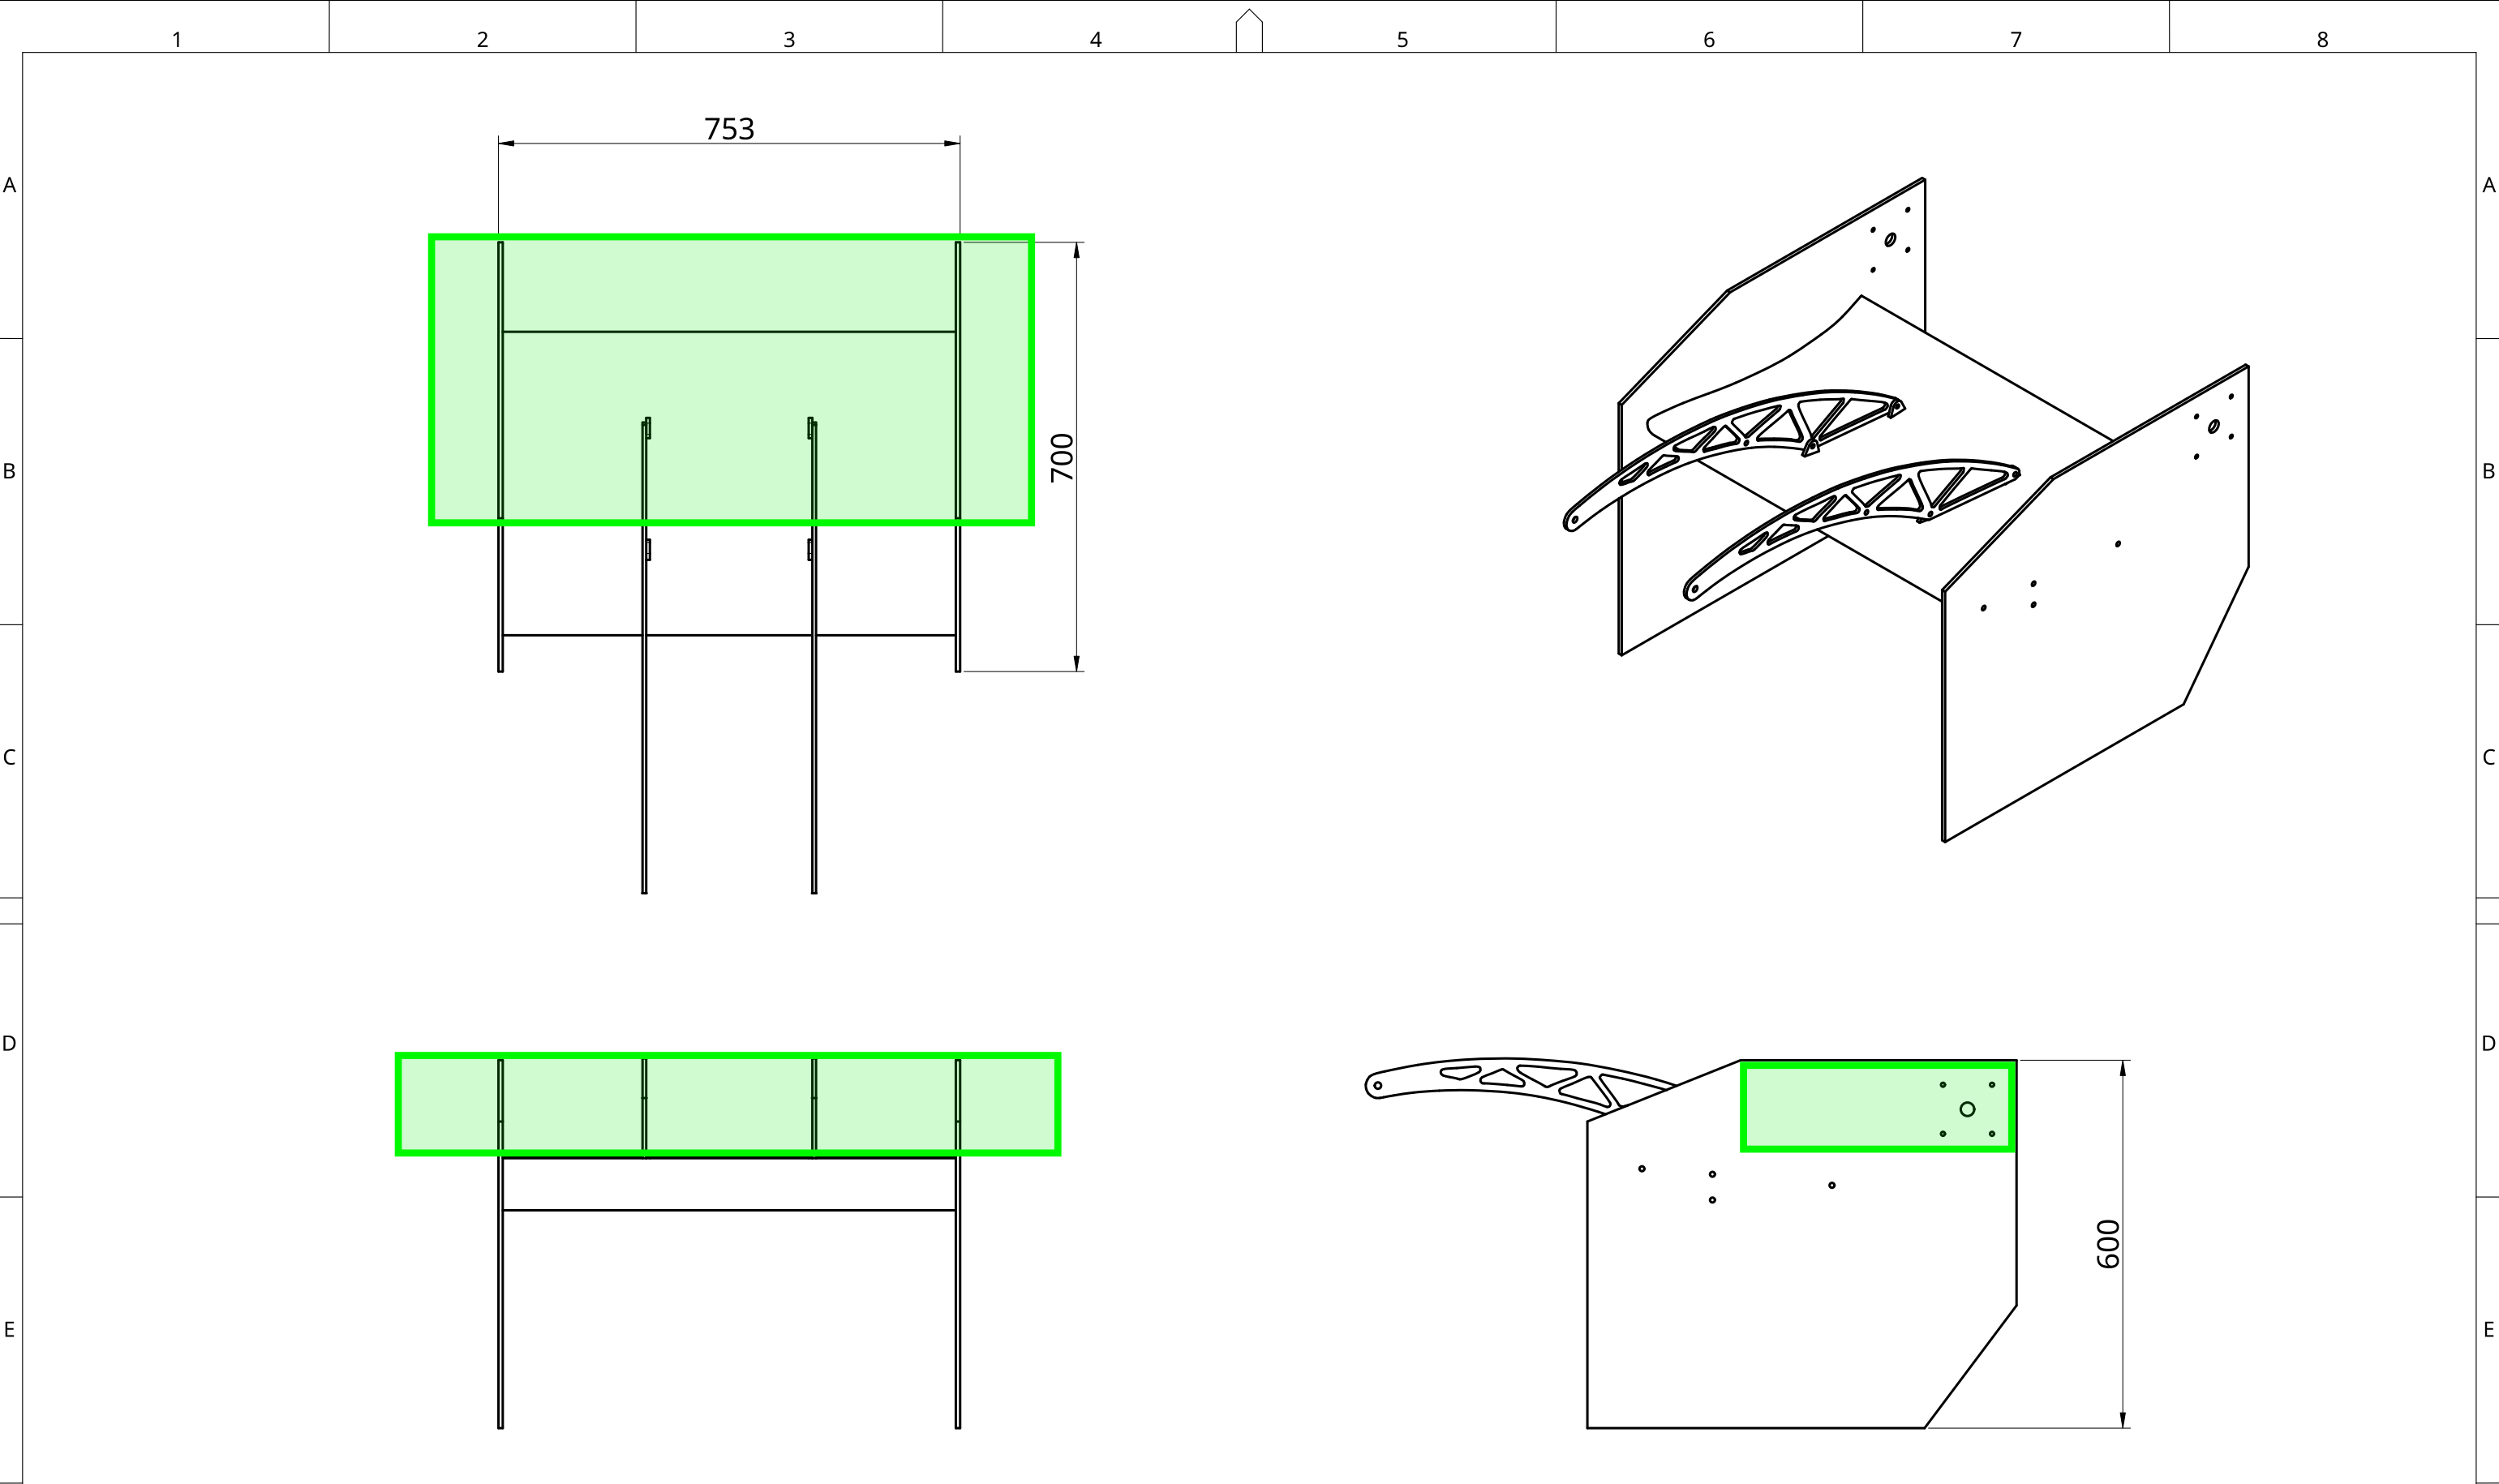


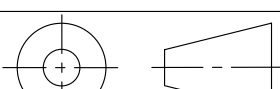

DEBUR ALL SHARP EDGES																																							
CONTINUOUS 6mm FILLET WELD UNLESS OTHERWISE STATED																																							
NOTICE THE TECHNICAL INFORMATION CONTAINED HEREIN IS CONSIDERED THE UNIVERSITY OF NEWCASTLE PROPERTY AND SHALL NOT BE USED, REPRODUCED, RELEASED OR DISCLOSED IN WHOLE OR PART WITHOUT WRITTEN PERMISSION.					THE UNIVERSITY OF NEWCASTLE COLLEGE OF ENGINEERING, SCIENCE AND ENVIRONMENT SCHOOL OF ENGINEERING - DISCIPLINE OF AEROSPACE, MECHANICAL & MECHATRONICS ENGINEERING ENGINEERING CLOSE, CALLAGHAN NSW 2308 FOR ENQUIRIES PLEASE CONTACT SENIOR MECHANICAL ENGINEER EMAIL: michael.j.carr@newcastle.edu.au		 THE UNIVERSITY OF NEWCASTLE AUSTRALIA	 DRAWN TO AS1100-1992 ALL DIMENSIONS IN MILLIMETRES UNLESS OTHERWISE STATED DO NOT SCALE CAD GENERATED DRAWING DO NOT MANUALLY UPDATE		TOLERANCES LINEAR 0.±0.50 0.0±0.10 0.00±0.05 ANGULAR 0.±0.20DEG 0.0±0.15DEG 0.00±0.10DEG	TITLE: NU16 REAR WING <table><tr><td>PROJECT NO.:</td><td>APPV'D</td><td></td><td></td><td></td><td>DRAWING NO.:</td></tr><tr><td>FINISH: 3.2 / UOS</td><td>CHK'D</td><td></td><td></td><td></td><td>REVISION:</td></tr><tr><td>QUANTITY:</td><td>DRAWN</td><td>JYE HOLLIER</td><td></td><td>2023-07-11</td><td>SCALE: 1:10</td></tr><tr><td>MATERIAL: N/A</td><td></td><td>NAME</td><td>SIGNATURE</td><td>DATE</td><td>SHEET: 1/2 A3</td></tr></table>					PROJECT NO.:	APPV'D				DRAWING NO.:	FINISH: 3.2 / UOS	CHK'D				REVISION:	QUANTITY:	DRAWN	JYE HOLLIER		2023-07-11	SCALE: 1:10	MATERIAL: N/A		NAME	SIGNATURE	DATE	SHEET: 1/2 A3
PROJECT NO.:	APPV'D				DRAWING NO.:																																		
FINISH: 3.2 / UOS	CHK'D				REVISION:																																		
QUANTITY:	DRAWN	JYE HOLLIER		2023-07-11	SCALE: 1:10																																		
MATERIAL: N/A		NAME	SIGNATURE	DATE	SHEET: 1/2 A3																																		
REVISIONS																																							
1					2																																		
3					4																																		
5					6																																		
7					8																																		